


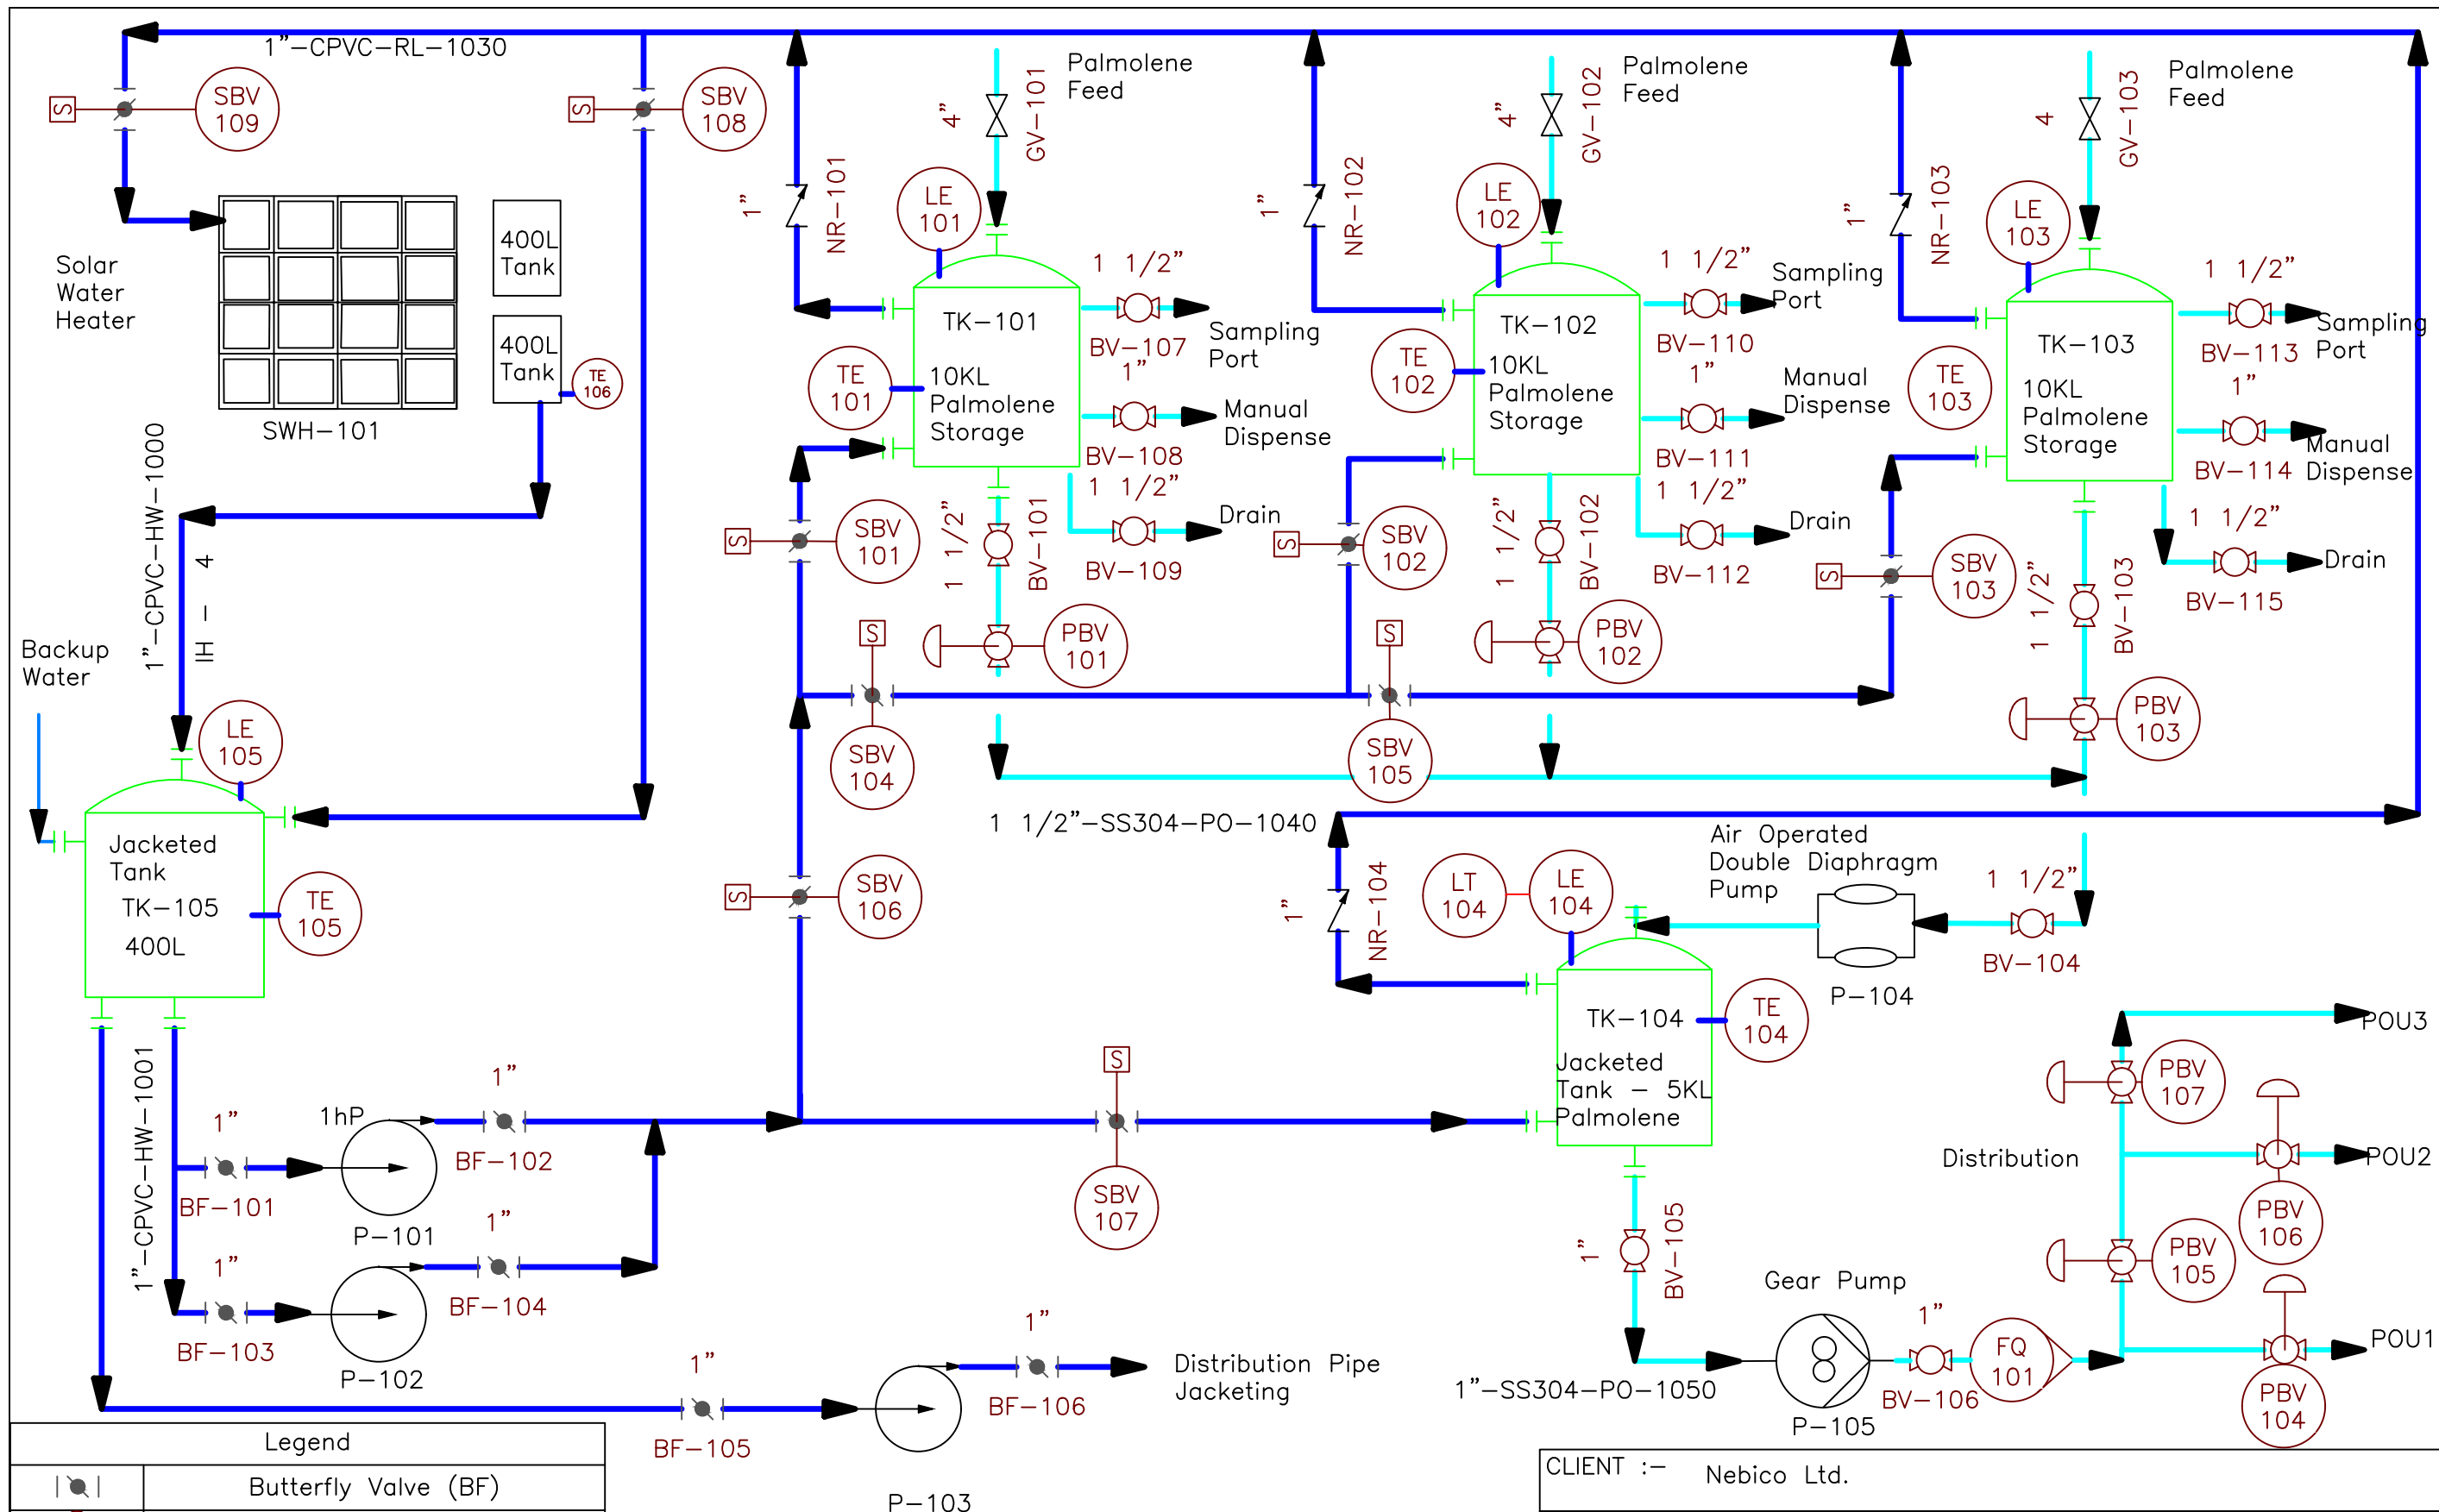

Legend	
	Butterfly Valve (BF)
	Pneumatic Ball Valve (PBV)
	Gate Valve
	Solenoid Butterfly Valve (SBV)
	Non-Return Valve (NR)
	Flow Meter
	Ball Valve (BV)
	Temperature/Level Element

Legend	
SWH	Solar Water Heater
	Palmolene Oil Line
	Hot Water Line

CLIENT :- Nebico Ltd.	
TITLE :- Palmoline Oil Storage and Distribution System	
MECHATRONICS ENGINEERING PVT. LTD. New Baneshwor-10, Kathmandu, Nepal Tel: - +977 1 5245074, +977 9851217249 Email: pramod@meplnepal.com	
Drawn By :- Sandesh Ghorsai	Drawing No:- 1 of 1
Checked By :- Pramod Neupane	Sheet No:- 1
Approved By :-	PROJECT NO :-