


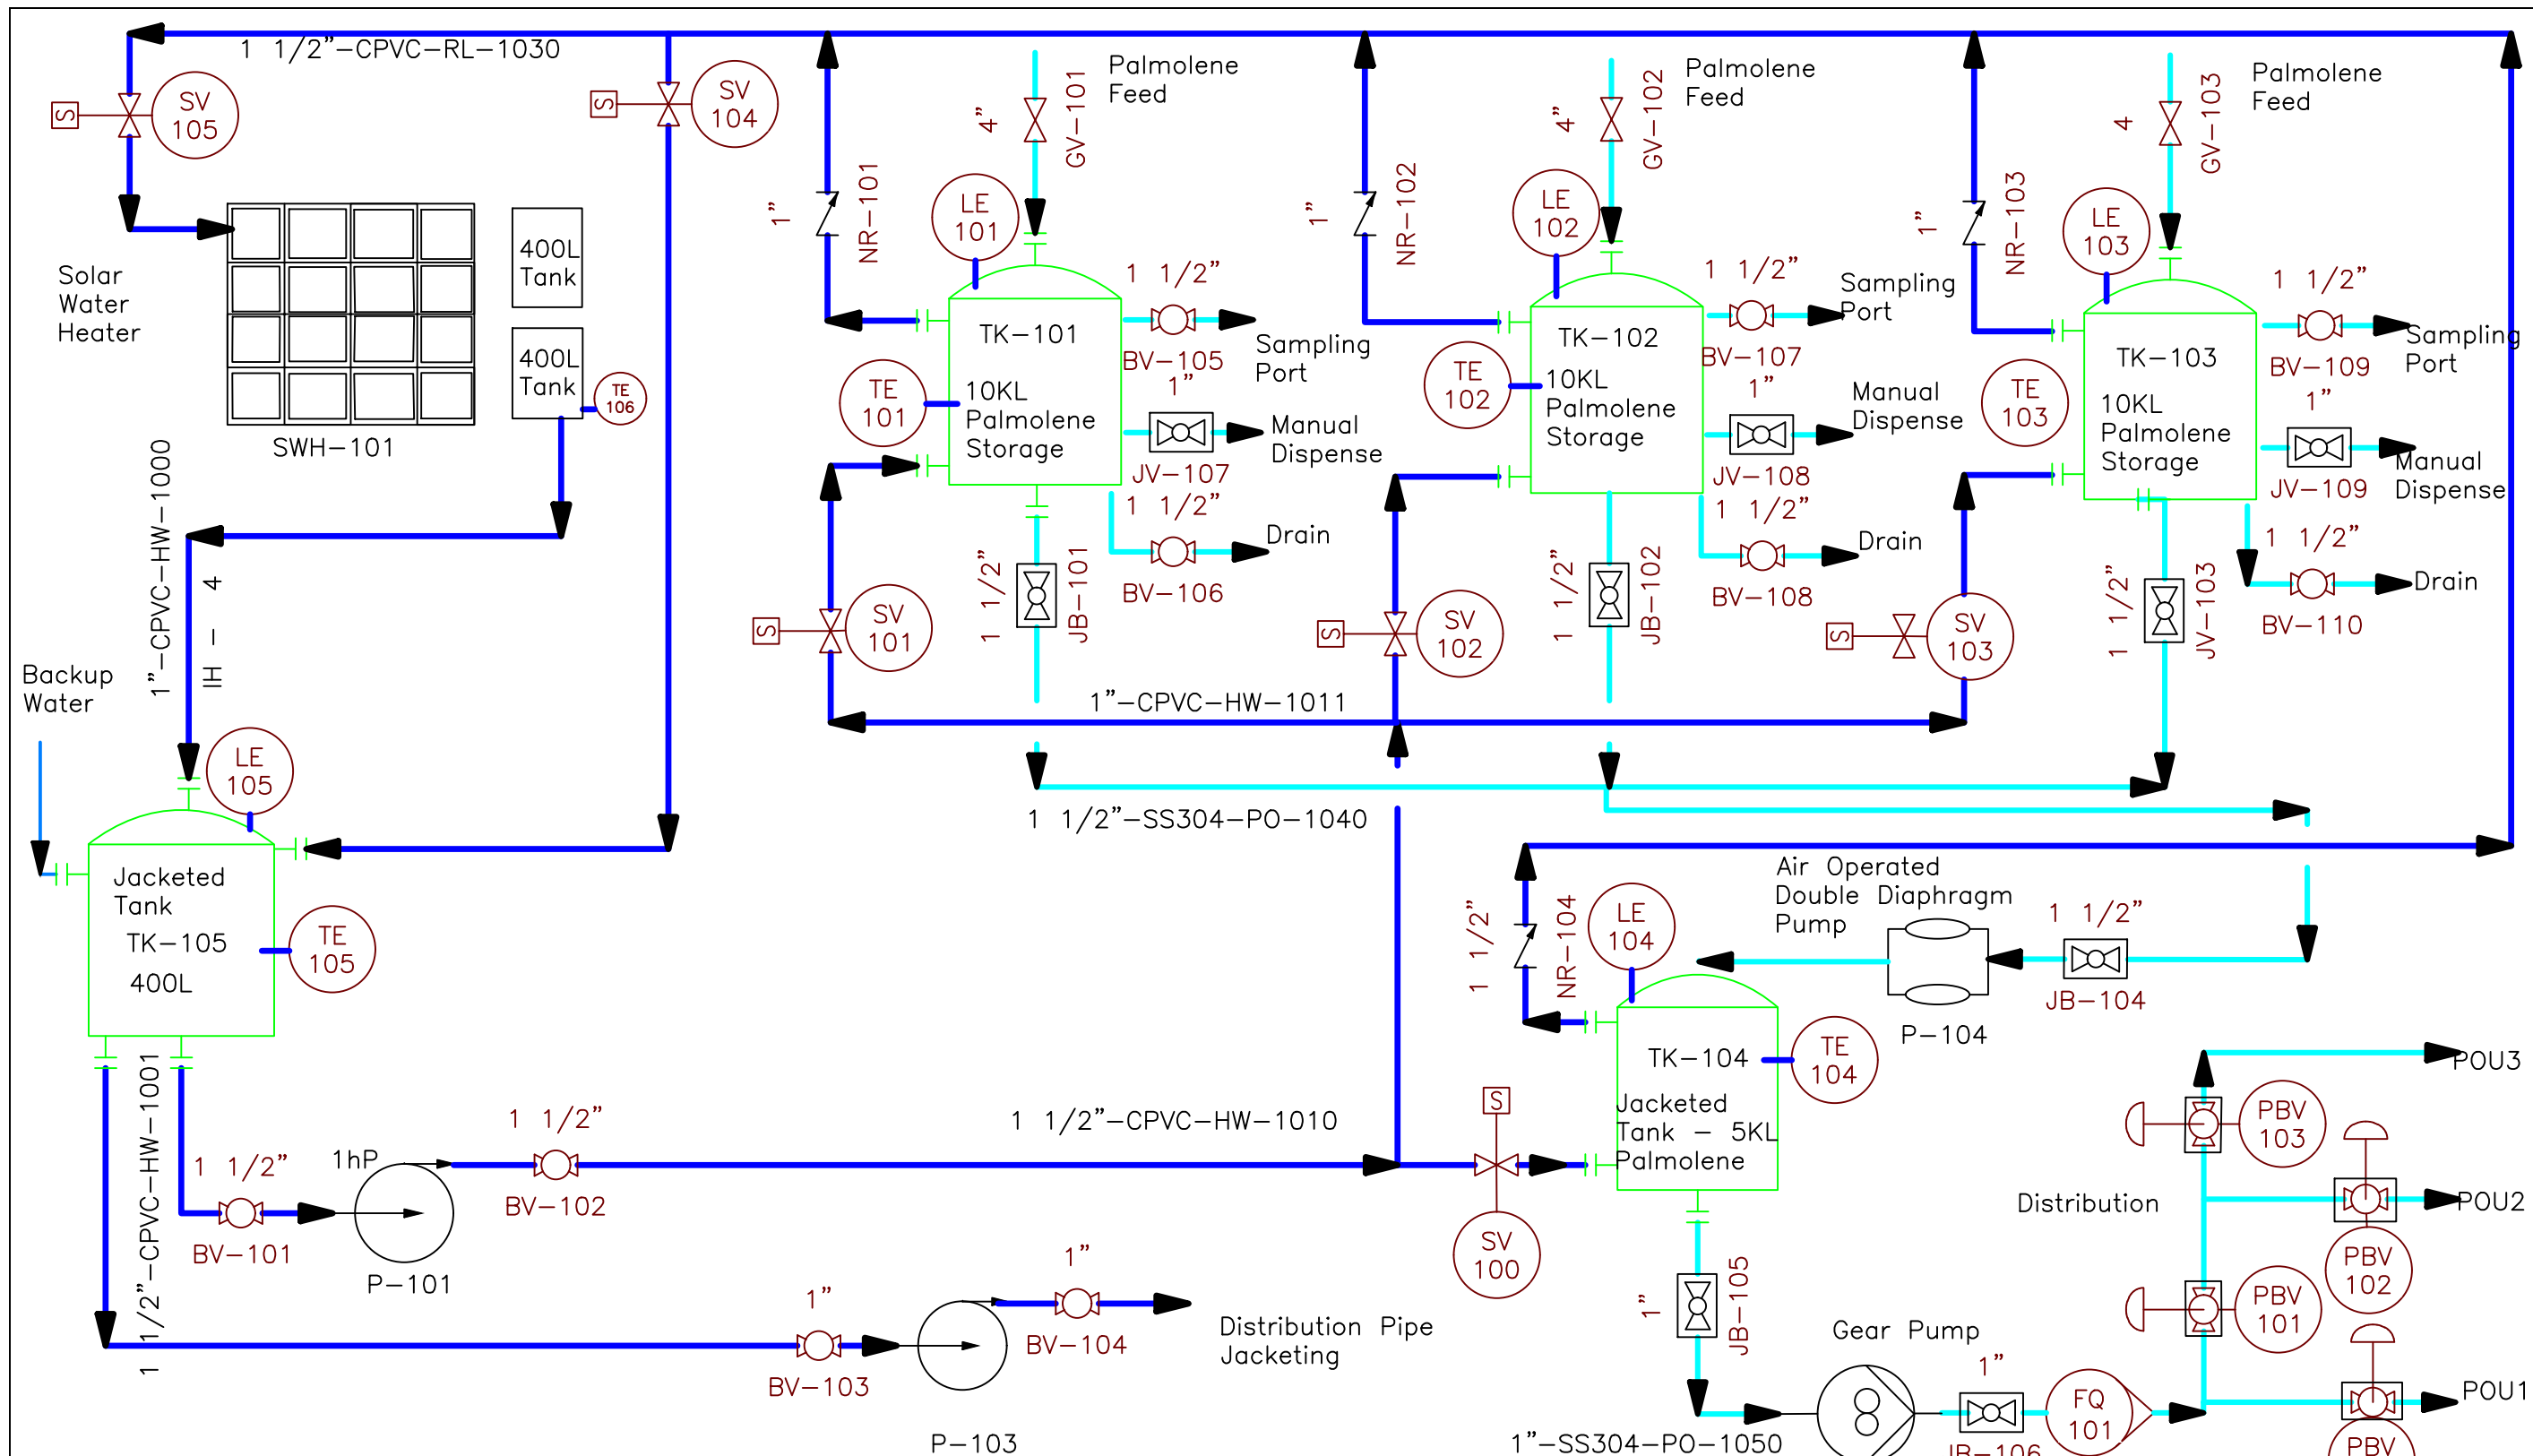

Legend				
	Manual Ball Valve (BV)	4-1"CPVC	6-1.5"SS	10
	Pneumatic Jacketed Ball Valve(PBV)	4-1"SS		4
	Gate Valve (GV)	3-4"SS		3
	Direct Operated Solenoid Valve(SV)	6-1"		6
	Non-Return Valve (NR)	4-1"CPVC		4
	Flow Meter (FQ)	1		1
	Jacketed Manual Ball Valve (JV)	5-1"SS	4-1.5"SS	9
TE/LE	Temperature/Level Element	6-5		6-5

Legend	
SWH	Solar Water Heater
	Palmolene Oil Line
	Hot Water Line

CLIENT :- Nebico Ltd.		
TITLE :- Palm Oil Storage and Distribution System		
MECHATRONICS ENGINEERING PVT. LTD. New Baneshwor-10, Kathmandu, Nepal Tel: - +977 1 5245074, +977 9851217249 Email: pramod@mepnepal.com		
Drawn By :-	Sandesh Ghorsai	Drawing No:- 1 of 1
Checked By :-	Pramod Neupane	Sheet No:- 1
Approved By :-		PROJECT NO :-